
PLANTA DE ARQUITETURA

RIVIERA MARTIM DE SÁ
FINAIS 2 E 5

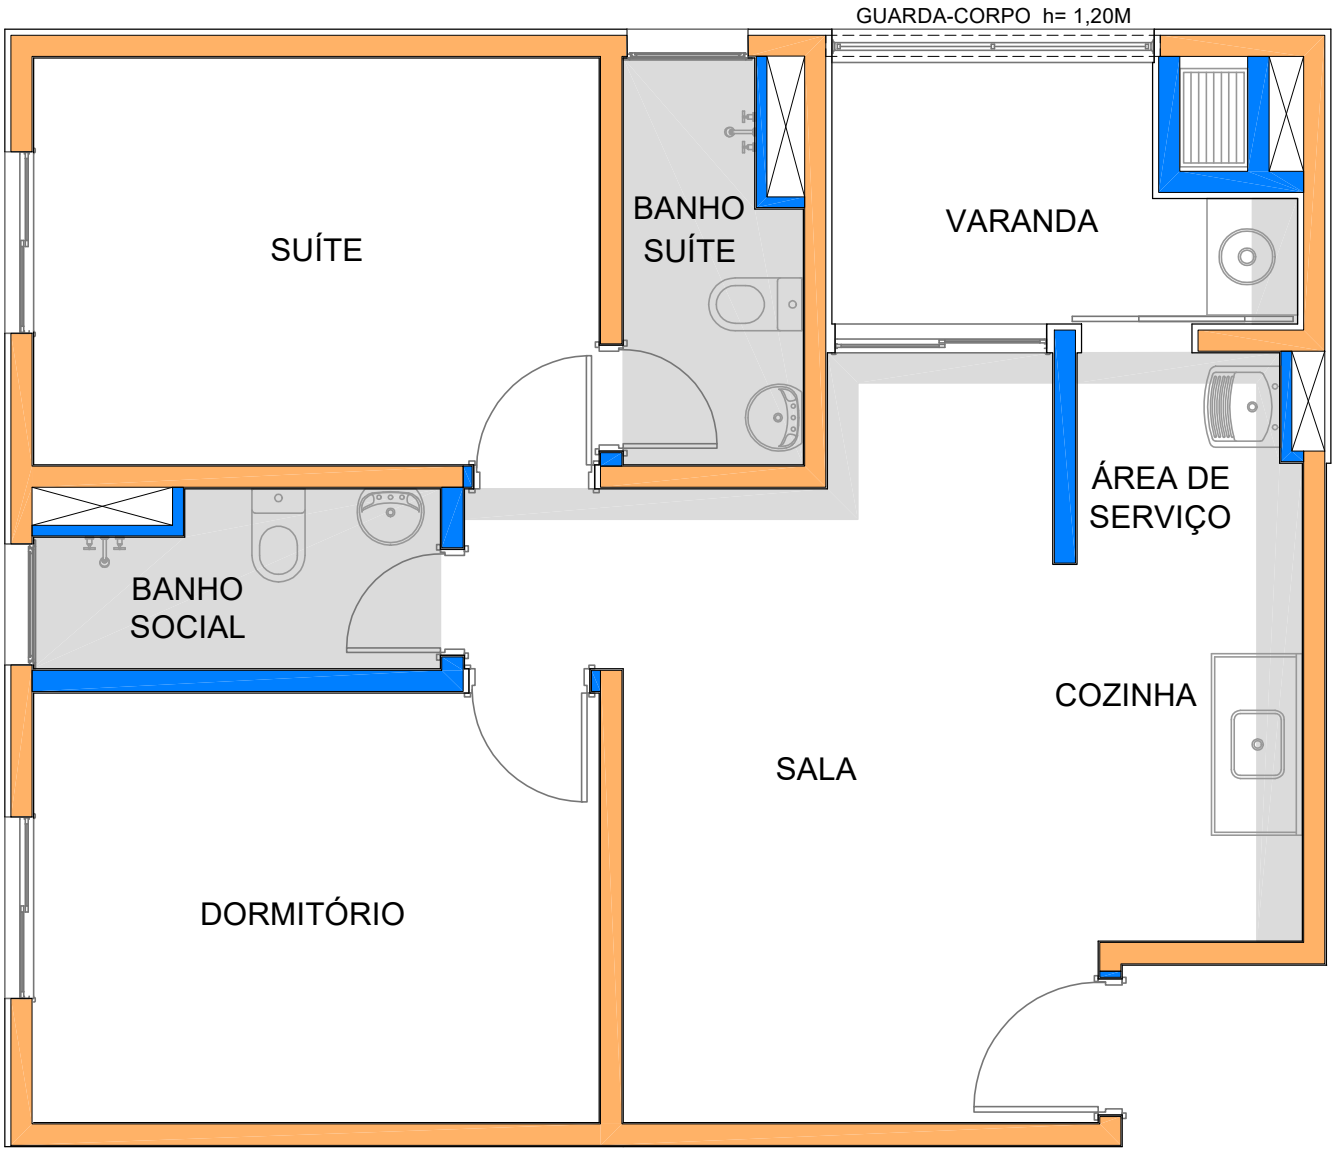

LEGENDA

ESCALA: 1 : 50


- ÁREAS COM FORRO / SANCA DE GESSO
- ALVENARIA ESTRUTURAL
- PAREDE DRYWALL
- PROJEÇÃO
- VAZIO / SHAFT HIDRÁULICO

ATENÇÃO!!

EM FUNÇÃO DAS CARACTERÍSTICAS ESTRUTURAIS DO EMPREENDIMENTO (**ALVENARIA ESTRUTURAL**), É PROIBIDA A EXECUÇÃO DE REFORMAS OU ALTERAÇÕES NAS UNIDADES QUE ENVOLVAM A REMOÇÃO, MODIFICAÇÃO OU ABERTURA DE VÃOS NAS ALVENARIAS ESTRUTURAIS, INCLUSIVE RASGOS NAS PAREDES PARA INSTALAÇÃO EMBUTIDA DE TUBULAÇÕES HIDRÁULICAS E/OU ELÉTRICAS.

PLANTA DE ELÉTRICA

RIVIERA MARTIM DE SÁ
FINAIS 2 E 5

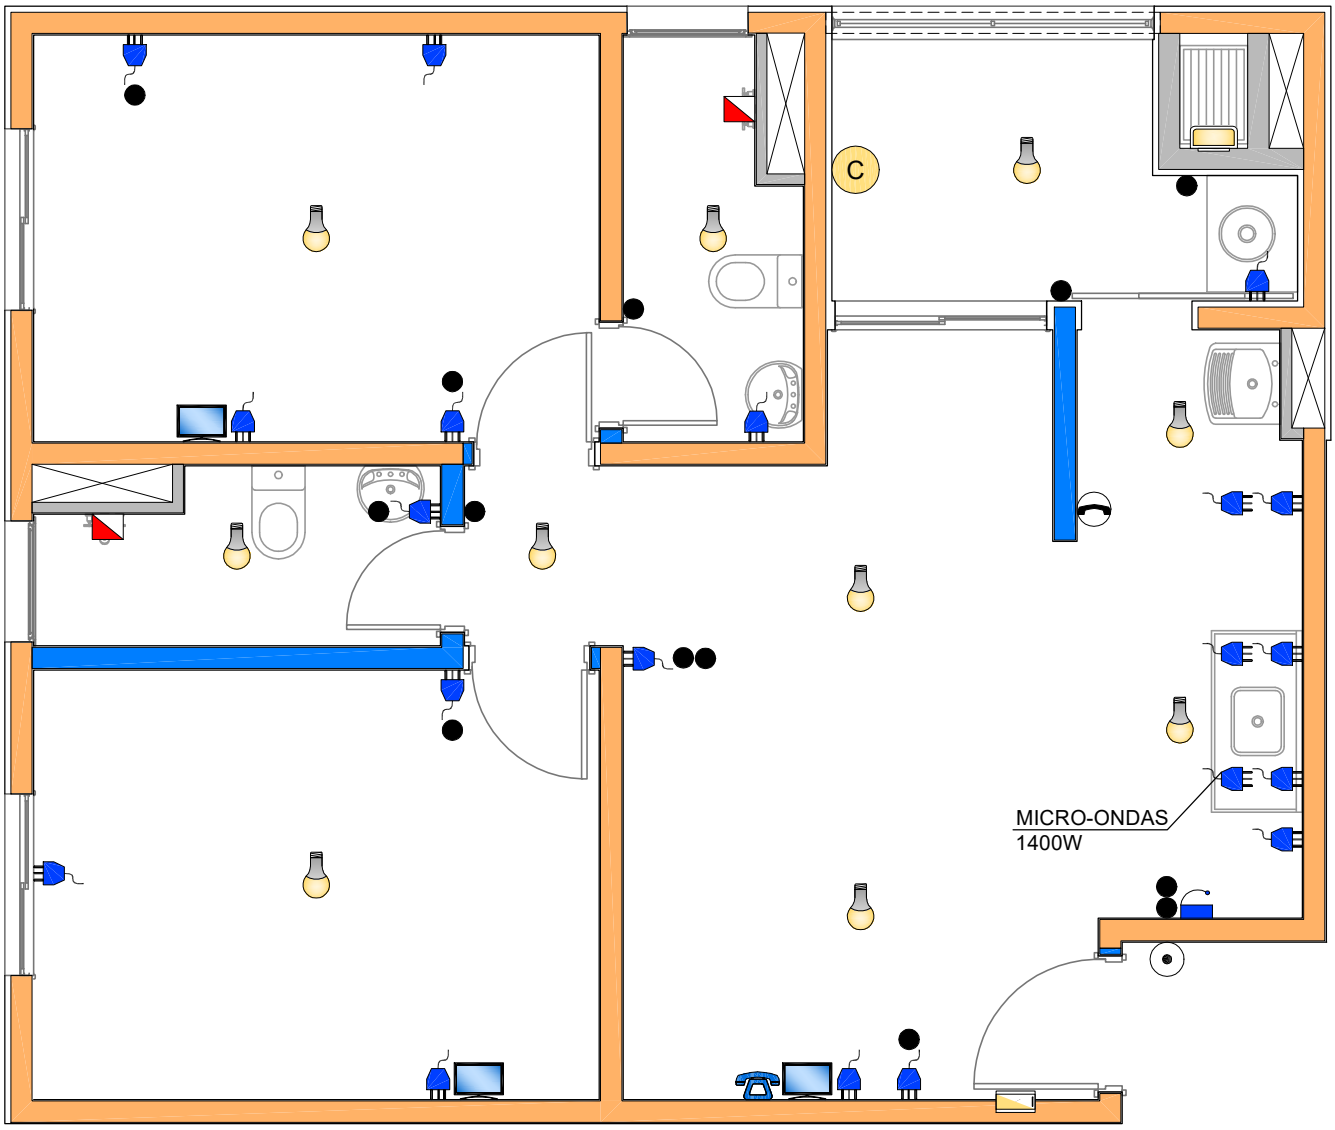

OBSERVAÇÃO IMPORTANTE!
- NÃO EXECUTE FUROS NA REGIÃO DO QUADRO DE LUZ E FORÇA/SISTEMAS;
- AO FURAR AS PAREDES, OBEDEÇA UMA FAIXA DE SEGURANÇA DE 20 cm EM TORNO DE TOMADAS E INTERRUPTORES, INCLUSIVE OBEDEÇA ESSA FAIXA DE SEGURANÇA NO ALINHAMENTO DO PISO AO TETO.

LEGENDA

- PONTO PARA ILUMINAÇÃO DE TETO
- BOTÃO DA CAMPAINHA
- PONTO PARA CHUVEIRO ELÉTRICO 220V
- QUADRO DE LUZ E FORÇA
- PONTO PARA ILUMINAÇÃO NA PAREDE (ARANDELA)
- INTERRUPTOR DE LUZ
- PONTO PARA INTERFONE
- PONTO PARA TELEFONE
- TOMADA 220V
- CAMPAINHA DE PAREDE
- C — PONTO PARA CONDENSADORA (AR CONDICIONADO)
- PONTO PARA TV

ATENÇÃO: É PROIBIDA A ABERTURA DE VÃOS NAS **ALVENARIAS ESTRUTURAIS**, INCLUSIVE RASGOS NAS PAREDES PARA INSTALAÇÃO EMBUTIDA DE TUBULAÇÕES HIDRÁULICAS E/OU ELÉTRICAS.

QUADRO DE LUZ E FORÇA

RIVIERA MARTIM DE SÁ
FINAIS 1, 2, 3, 4, 5 E 6


CIRCUITO	DESCRIÇÃO	CORRENTE (A)	CARGA MÁXIMA POR CIRCUITO POTÊNCIA (W)	TENSÃO (V)
1	ILUMINAÇÃO GERAL	16	177	127
2	TOMADAS SUÍTE, DORMITÓRIO E SALA	20	1300	220
3	TOMADAS BANHO SUÍTE E BANHOS SOCIAL	20	1200	220
4	TOMADAS COZINHA	20	1400	220
5	TOMADAS ÁREA DE SERVIÇO	20	600	220
6	TOMADAS ÁREA DE SERVIÇO E VARANDA	20	1200	220
7	CHUVEIRO	32	5400	220
8	CHUVEIRO	32	5400	220
9	AR CONDICIONADO	20	815	220
R	RESERVA	-	-	-
R	RESERVA	-	-	-
R	RESERVA	-	-	-
R	RESERVA	-	-	-

OBSERVAÇÃO IMPORTANTE!
1) NÃO EXECUTE FUROS NA REGIÃO DO QUADRO DE LUZ E FORÇA;
2) AO FURAR AS PAREDES, OBEDEÇA UMA FAIXA DE SEGURANÇA DE 20cm EM TORNO DE TOMADAS E INTERRUPTORES, DO PISO AO TETO;
3) O EQUIPAMENTO COM CIRCUITO EXCLUSIVO **DEVERÁ SER ADQUIRIDO E INSTALADO PELO PROPRIETÁRIO NO PONTO ELÉTRICO ESPECÍFICO, CONFORME PLANTA DE ELÉTRICA**;
4) NÃO ULTRAPASSE A CARGA MÁXIMA ADMISSÍVEL DE CADA CIRCUITO.

ATENÇÃO: É PROIBIDA A ABERTURA DE VÃOS NAS **ALVENARIAS ESTRUTURAIS**, INCLUSIVE RASGOS NAS PAREDES PARA INSTALAÇÃO EMBUTIDA DE TUBULAÇÕES HIDRÁULICAS E/OU ELÉTRICAS.

PLANTA DE AR CONDICIONADO, GÁS E PRUMADAS

RIVIERA MARTIM DE SÁ
FINAIS 2 E 5

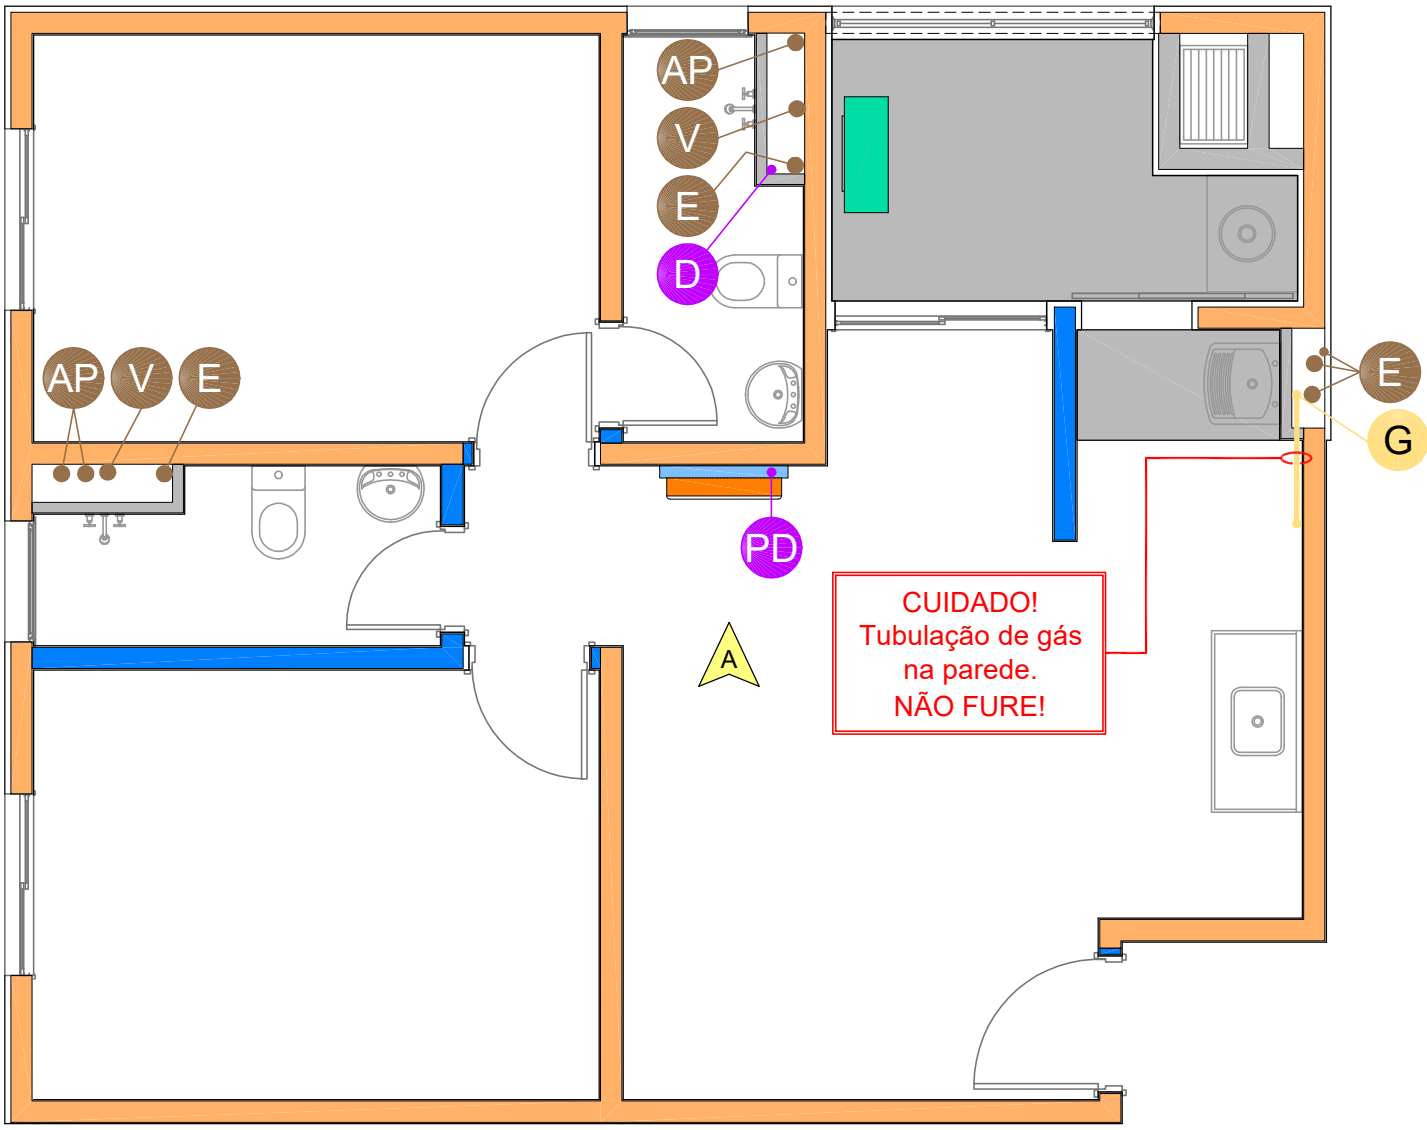

LEGENDA

PRUMADAS

- V — VENTILAÇÃO
- E — ESGOTO
- AP — ÁGUA PLUVIAL
- D — DRENO
- G — GÁS

PONTOS

- PD — DRENO
- VISTAS

TUBULAÇÃO DE GÁS NO PISO

LOCAL PREVISTO P/ INSTALAÇÃO DA CONDENSADORA DE AR CONDICIONADO

LOCAL PREVISTO P/ INSTALAÇÃO DA EVAPORADORA DE AR CONDICIONADO DE PAREDE


OBSERVAÇÕES:

1. NÃO EXECUTE FUROS NA REGIÃO DAS PRUMADAS;
2. USE LIMITADOR DE BROCA E NÃO ULTRAPASSE 2 CM DE PROFUNDIDADE;
3. OBEDEÇA A FAIXA DE SEGURANÇA INDICADA NAS VISTAS NO ALINHAMENTO DO PISO AO TETO;
4. OS ENCANAMENTOS QUE PASSAM POR UMA PAREDE HIDRÁULICA PASSAM POR ESTA MESMA PAREDE NO LADO OPOSTO. **CUIDADO NA INSTALAÇÃO DA MARCENARIA;**
5. **NÃO FURE SANCAS E OS FORROS DE GESSO**, POIS ELES ABRIGAM DUTOS E TUBULAÇÕES.


NÃO FURE AS ÁREAS INDICADAS NA COR CINZA

ESQUEMA DE DRENO

RIVIERA MARTIM DE SÁ
FINAIS 2 E 5
SALA

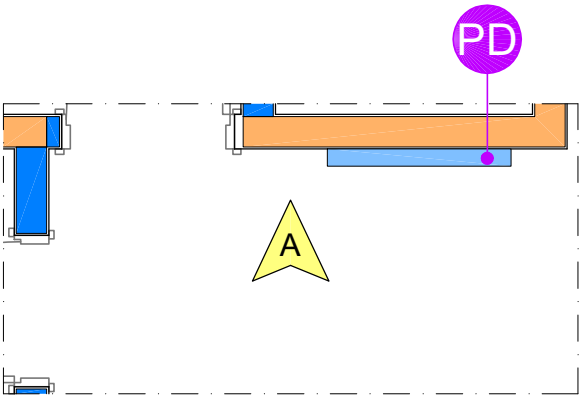

PLANTA

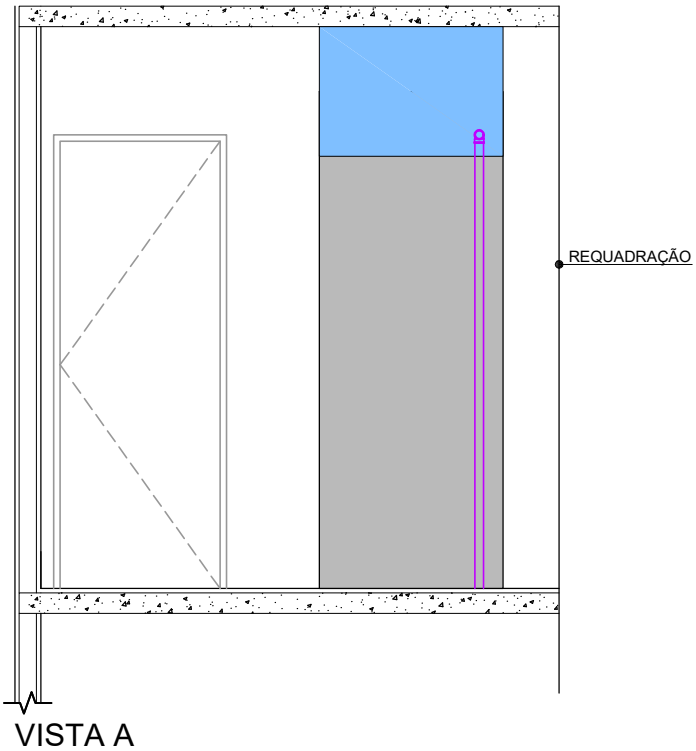

VISTA A

LEGENDA

PRUMADA / DESCIDA

D DRENO

PONTOS

PD DRENO

TUBULAÇÕES

DRENO

OBSERVAÇÕES:
AS MEDIDAS INDICADAS NAS VISTAS ESTÃO EM CENTÍMETROS.

ANTES DE FURAR:
USAR LIMITADOR DE BROCA E NÃO ULTRAPASSAR 2 CM DE PROFUNDIDADE.
LEMBRE-SE QUE OS ENCANAMENTOS QUE PASSAM NA PAREDE ACIMA TAMBÉM ESTÃO PASSANDO POR ESTA MESMA PAREDE NO LADO OPOSTO.
CONSULTE A PLANTA DE PRUMADAS.
NÃO FURE AS SANCAS E OS FORROS DE GESSO, POIS ELES TAMBÉM ABRIGAM DUTOS OU TUBULAÇÕES.


NÃO FURAR NAS ÁREAS INDICADAS NA COR CINZA

CONCRETO


VISTA

ESQUEMA HIDRÁULICO

RIVIERA MARTIM DE SÁ
FINAIS 2 E 5
BANHO SUÍTE

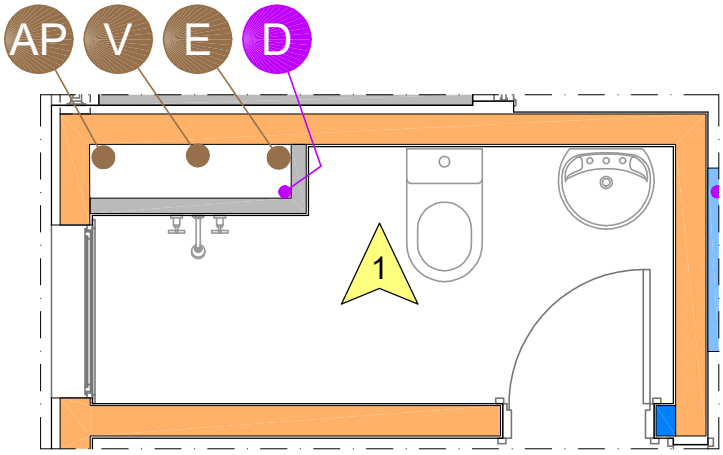

PLANTA

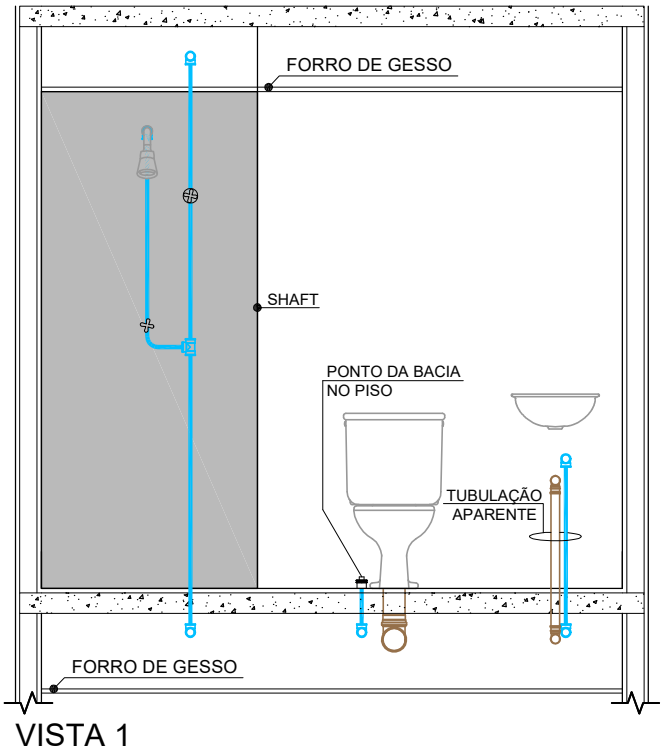

VISTA 1

LEGENDA

PRUMADAS / DESCIDAS

- V — VENTILAÇÃO
- E — ESGOTO
- AP — ÁGUA PLUVIAL
- G — GÁS

PONTOS

- PD — DRENO

TUBULAÇÕES

- ESGOTO
- GÁS
- ÁGUA FRIA (PEX)

OBSERVAÇÕES:

NAS MEDIDAS ACIMA, USE COMO REFERÊNCIA AS ESQUADRIAS E OS PONTOS APARENTES DE ÁGUA, GÁS, ESGOTO E REGISTROS.
AS MEDIDAS INDICADAS NAS VISTAS ESTÃO EM CENTÍMETROS.


ANTES DE FURAR:

USAR LIMITADOR DE BROCA E NÃO ULTRAPASSAR 2 CM DE PROFUNDIDADE.
LEMBRE-SE QUE OS ENCANAMENTOS QUE PASSAM NA PAREDE ACIMA TAMBÉM ESTÃO PASSANDO POR ESTA MESMA PAREDE NO LADO OPOSTO.
CONSULTE A PLANTA DE PRUMADAS.
NÃO FURE AS SANCAS E OS FORROS DE GESSO, POIS ELES TAMBÉM ABRIGAM DUTOS OU TUBULAÇÕES.


- NÃO FURAR NAS ÁREAS INDICADAS NA COR CINZA
- CONCRETO
- VISTA

ESQUEMA HIDRÁULICO

RIVIERA MARTIM DE SÁ
FINAIS 2 E 5
BANHO SOCIAL

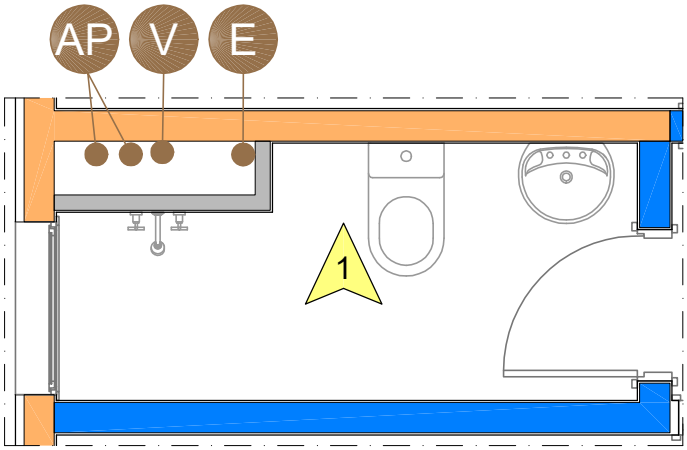

PLANTA

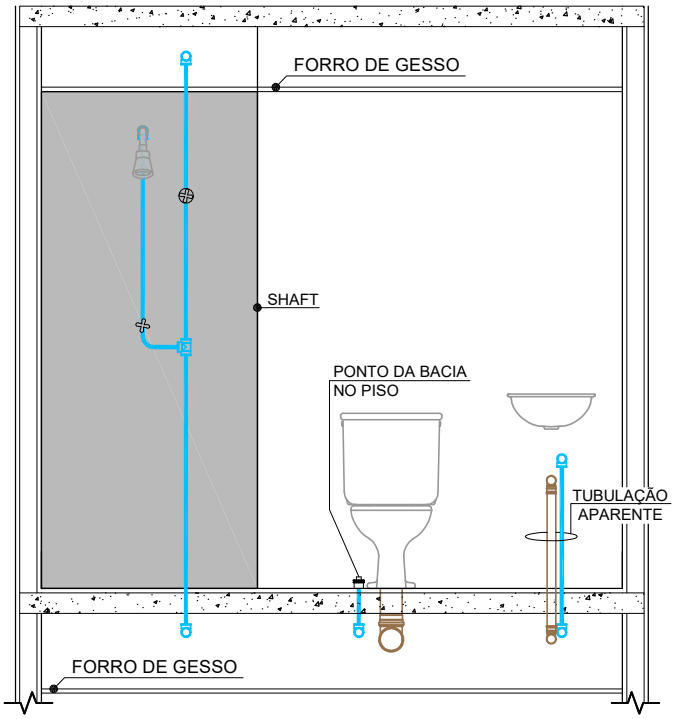

VISTA 1

LEGENDA

PRUMADAS / DESCIDAS

- V — VENTILAÇÃO
- E — ESGOTO
- AP — ÁGUA PLUVIAL
- G — GÁS

PONTOS

- PD — DRENO

TUBULAÇÕES

- ESGOTO
- GÁS
- ÁGUA FRIA (PEX)

OBSERVAÇÕES:

NAS MEDIDAS ACIMA, USE COMO REFERÊNCIA AS ESQUADRIAS E OS PONTOS APARENTES DE ÁGUA, GÁS, ESGOTO E REGISTROS.
AS MEDIDAS INDICADAS NAS VISTAS ESTÃO EM CENTÍMETROS.

ANTES DE FURAR:


USAR LIMITADOR DE BROCA E NÃO ULTRAPASSAR 2 CM DE PROFUNDIDADE.
LEMBRE-SE QUE OS ENCANAMENTOS QUE PASSAM NA PAREDE ACIMA TAMBÉM ESTÃO PASSANDO POR ESTA MESMA PAREDE NO LADO OPOSTO.
CONSULTE A PLANTA DE PRUMADAS.
NÃO FURE AS SANCAS E OS FORROS DE GESSO, POIS ELES TAMBÉM ABRIGAM DUTOS OU TUBULAÇÕES.

- NÃO FURAR NAS ÁREAS INDICADAS NA COR CINZA
- CONCRETO
- VISTA


ESQUEMA HIDRÁULICO

RIVIERA MARTIM DE SÁ
FINAIS 2 E 5
COZINHA E ÁREA DE SERVIÇO

CUIDADO!
Tubulação de gás na parede.
NÃO FURE!

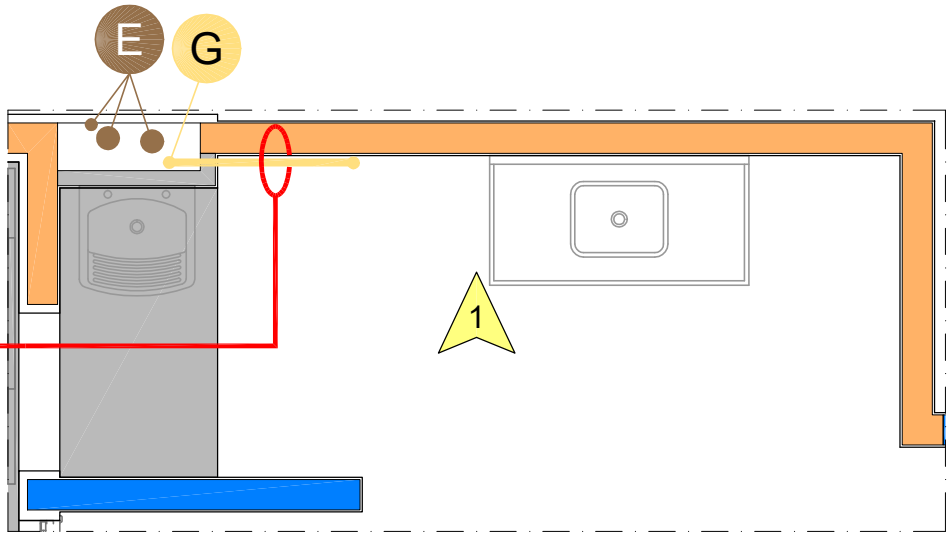

PLANTA

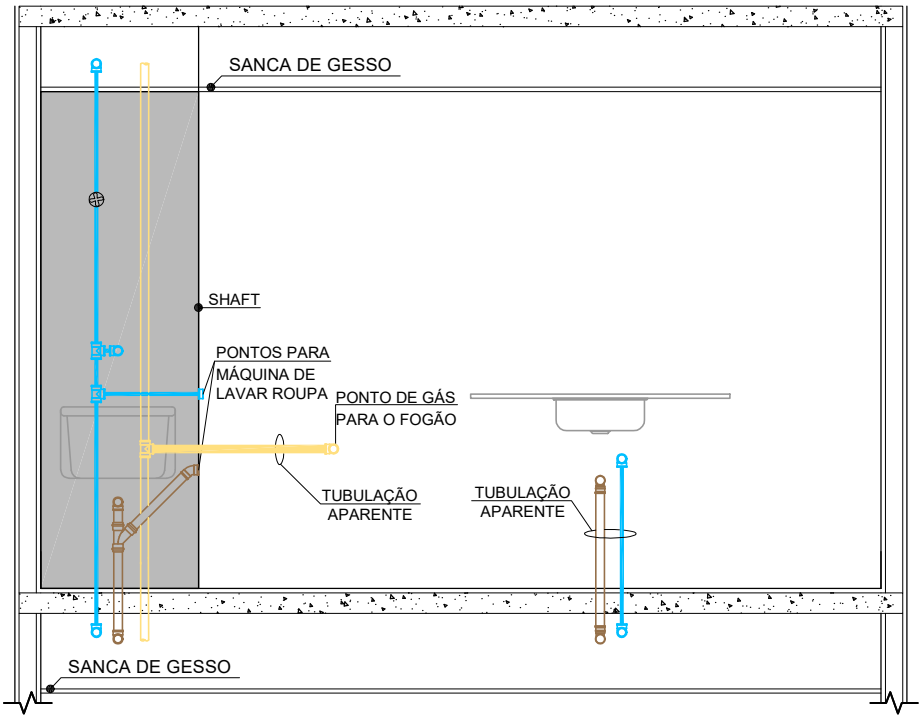

VISTA 1

LEGENDA

PRUMADAS / DESCIDAS
- V — VENTILAÇÃO
- E — ESGOTO
- AP — ÁGUA PLUVIAL
- G — GÁS

PONTOS
- PD — DRENO

TUBULAÇÕES
- ESGOTO
- GÁS
- ÁGUA FRIA (PEX)


OBSERVAÇÕES:
NAS MEDIDAS ACIMA, USE COMO REFERÊNCIA AS ESQUADRIAS E OS PONTOS APARENTES DE ÁGUA, GÁS, ESGOTO E REGISTROS.
AS MEDIDAS INDICADAS NAS VISTAS ESTÃO EM CENTÍMETROS.

ANTES DE FURAR:
USAR LIMITADOR DE BROCA E NÃO ULTRAPASSAR 2 CM DE PROFUNDIDADE.
LEMBRE-SE QUE OS ENCANAMENTOS QUE PASSAM NA PAREDE ACIMA TAMBÉM ESTÃO PASSANDO POR ESTA MESMA PAREDE NO LADO OPOSTO.
CONSULTE A PLANTA DE PRUMADAS.
NÃO FURE AS SANCAS E OS FORROS DE GESSO, POIS ELES TAMBÉM ABRIGAM DUTOS OU TUBULAÇÕES.


- NÃO FURAR NAS ÁREAS INDICADAS NA COR CINZA
- CONCRETO
- VISTA

ESQUEMA HIDRÁULICO

RIVIERA MARTIM DE SÁ
FINAIS 2 E 5
VARANDA

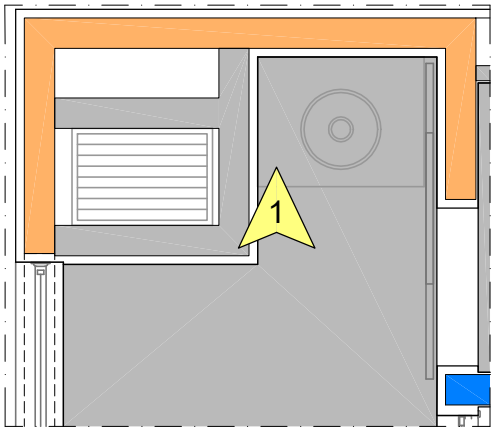

PLANTA

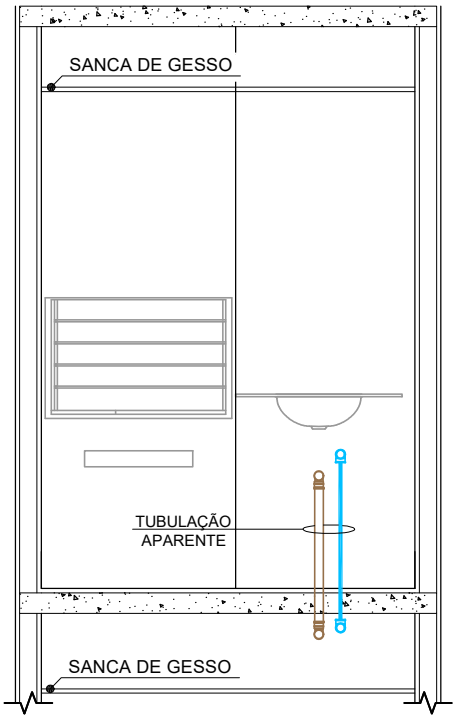

VISTA 1

LEGENDA

PRUMADAS / DESCIDAS

- V — VENTILAÇÃO
- E — ESGOTO
- AP — ÁGUA PLUVIAL
- G — GÁS

PONTOS

- PD — DRENO

TUBULAÇÕES

- ESGOTO
- GÁS
- ÁGUA FRIA (PEX)

OBSERVAÇÕES:
NAS MEDIDAS ACIMA, USE COMO REFERÊNCIA AS ESQUADRIAS E OS PONTOS APARENTES DE ÁGUA, GÁS, ESGOTO E REGISTROS.
AS MEDIDAS INDICADAS NAS VISTAS ESTÃO EM CENTÍMETROS.

ANTES DE FURAR:
USAR LIMITADOR DE BROCA E NÃO ULTRAPASSAR 2 CM DE PROFUNDIDADE.
LEMBRE-SE QUE OS ENCANAMENTOS QUE PASSAM NA PAREDE ACIMA TAMBÉM ESTÃO PASSANDO POR ESTA MESMA PAREDE NO LADO OPOSTO.
CONSULTE A PLANTA DE PRUMADAS.
NÃO FURE AS SANCAS E OS FORROS DE GESSO, POIS ELES TAMBÉM ABRIGAM DUTOS OU TUBULAÇÕES.

- NÃO FURAR NAS ÁREAS INDICADAS NA COR CINZA
- CONCRETO
- VISTA